


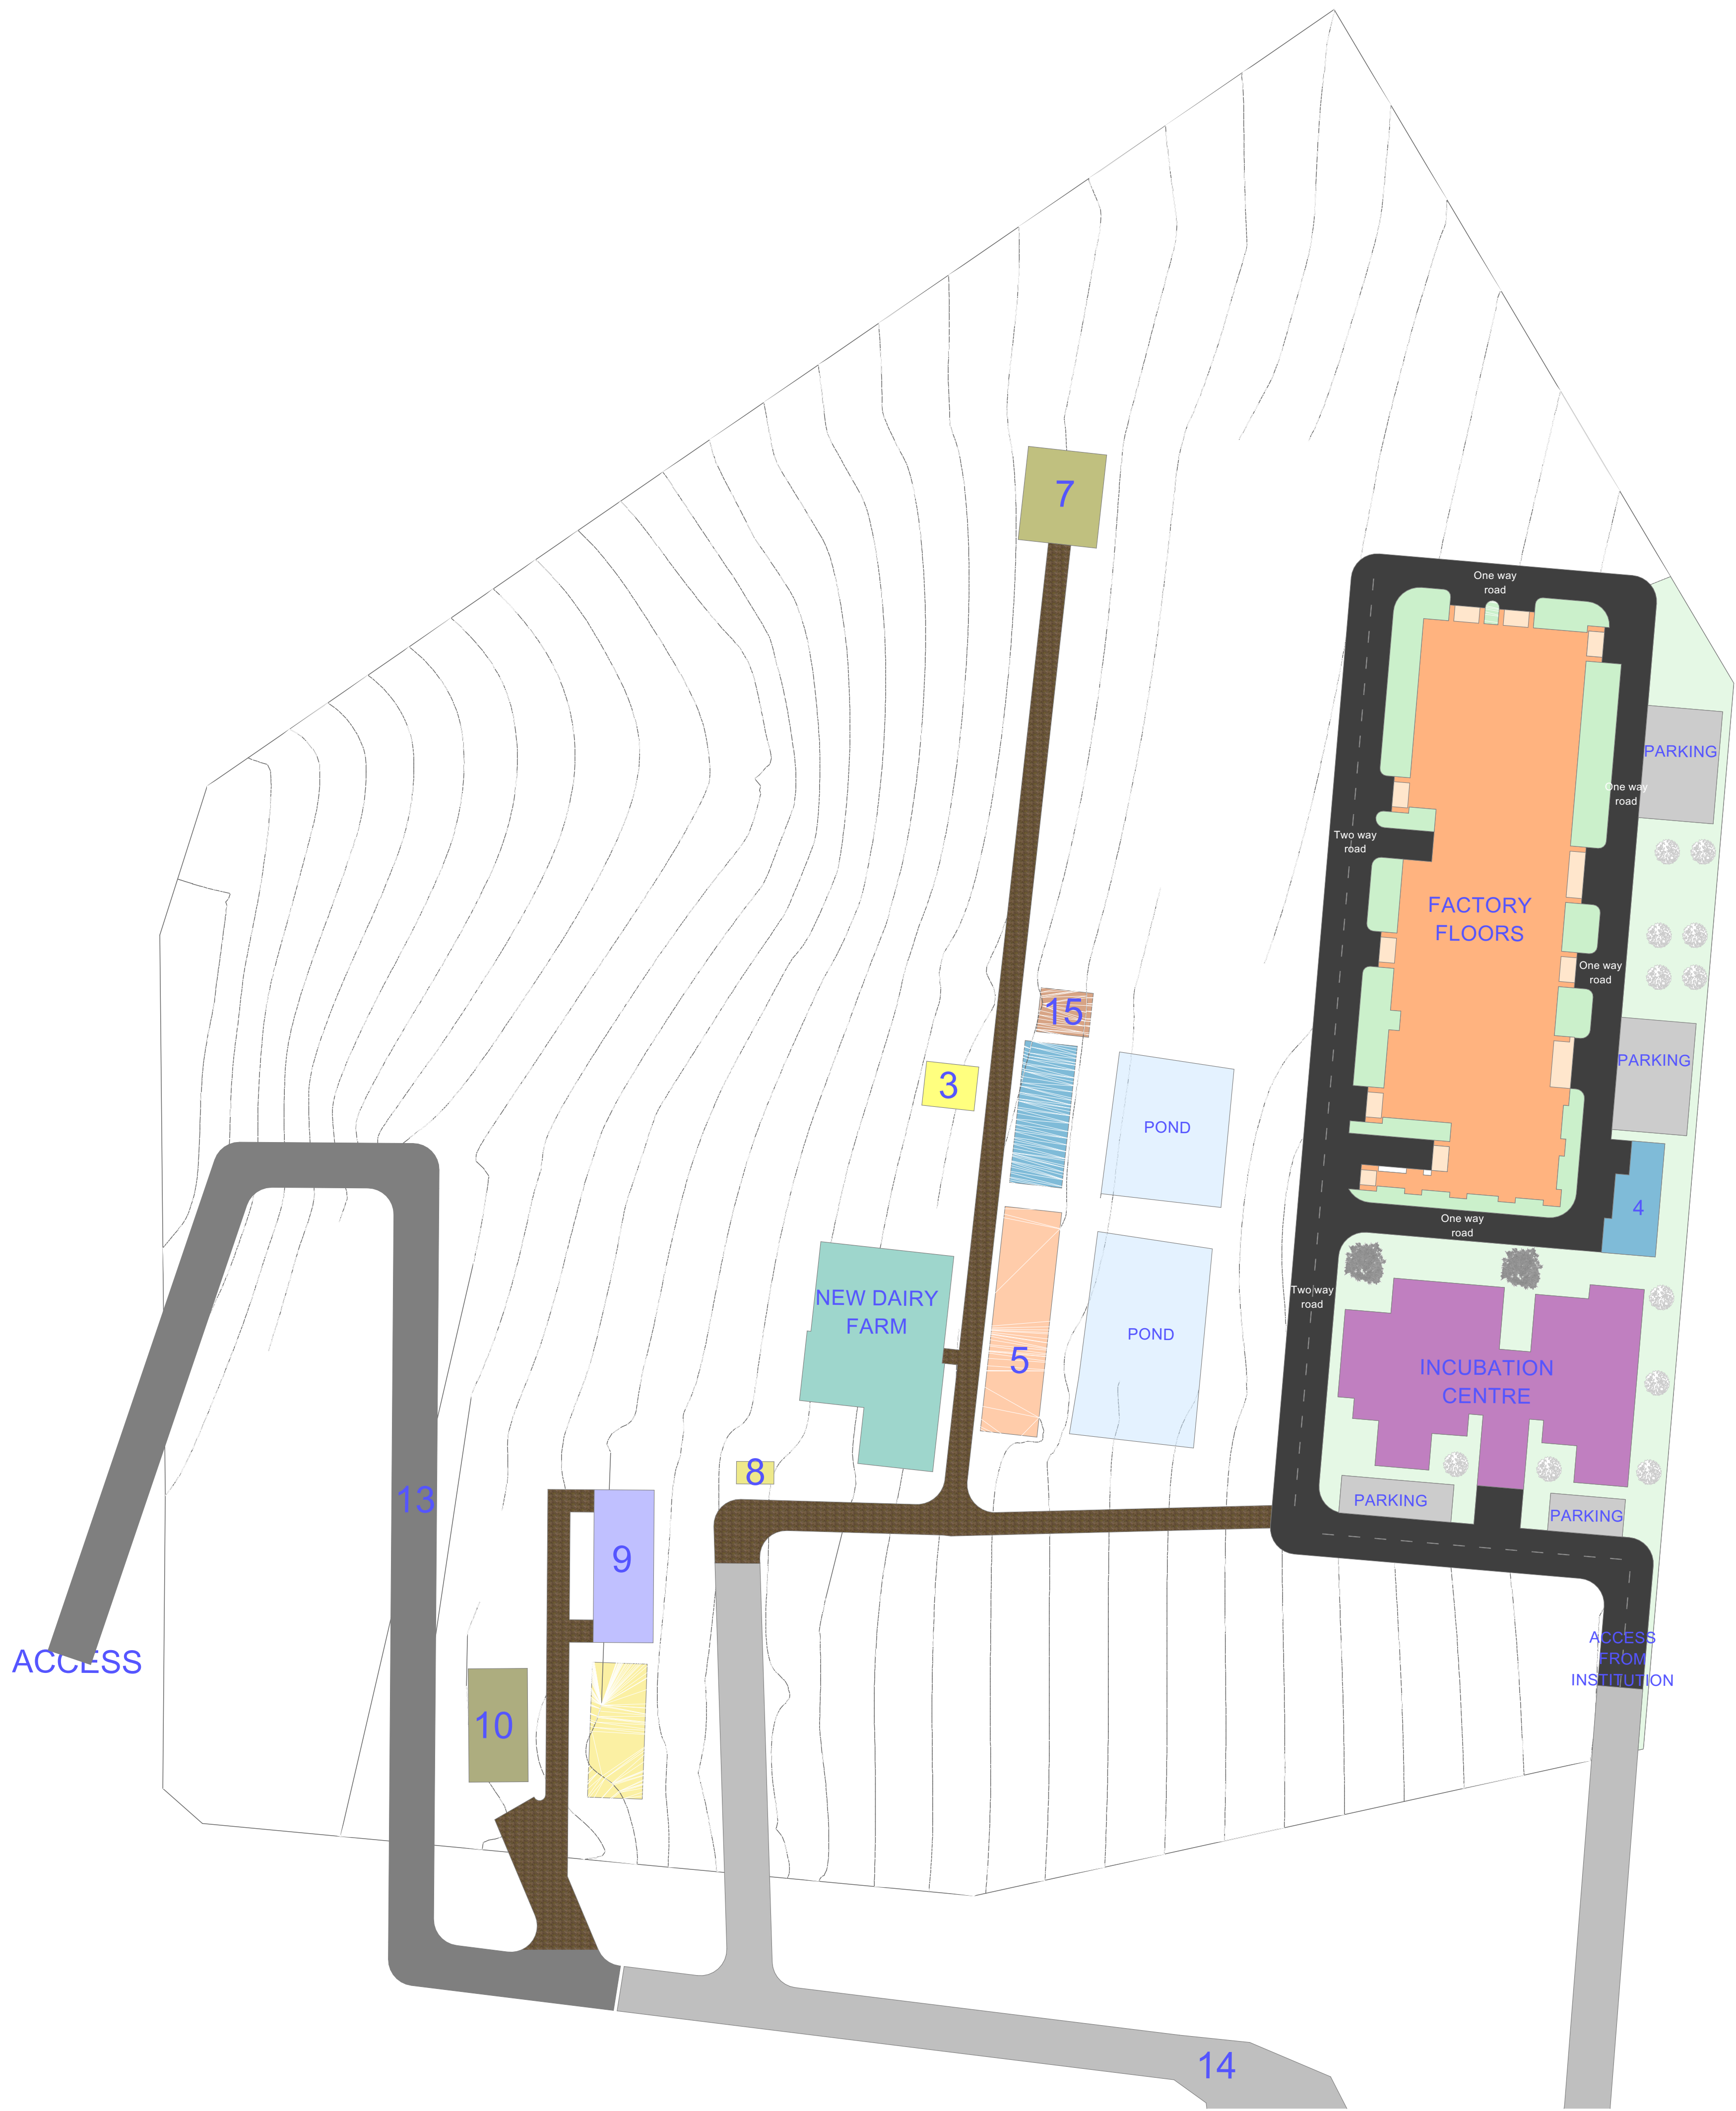

SITE PLAN

KEY	
	FACTORY FLOORS
	INCUBATION CENTRE
	CHANGING ROOM FOR WORKERS
	POWER HOUSE
	EXISTING DAIRY FARM
	NEW DAIRY FARM
	PIGGERY
	SITE HOUSE
	ANIMAL FEED PROCESSING FACTORY
	AGRICULTURAL ENGINEERING WORKSHOP
	PROPOSED LINK ROAD TO THE FACTORIES
	PEDESTRIAN AND ANIMAL PAVING
	PROPOSED LINK ROAD FROM NEW GATE
	EXISTING INSTITUTION ROAD

1:500

GENERAL NOTES

1. This drawing to be read in conjunction with Engineers' drawings.
2. All dimensions are in mm unless otherwise specified.
3. Drawings are not to be scaled . Only figured dimensions should be used.
4. The contractor must check and verify all dimensions before commencement of work and if necessary confirm with the architect.

CONSTRUCTION

Approved anti-termite treatment & 1000 gauge polythene sheeting cover to be provided under all ground floor concrete slab on compacted hardcore to approval.
DPC to be 3ply bituminous felt to be provided under all walls.

STRUCTURAL

1. All Black cotton soil to be removed from below all building and paved surfaces
2. All reinforced concrete work will be in accordance with structural drawings .
3. Foundation depths to be determined on site to S.E approval
4. All walls less than 200mm thick to be reinforced with hoop iron at every alternate course.
5. All adjacent R.C work and masonry walls to be tied with strap irons at every course

MECHANICAL

1. All Plumbing and Drainage Work to comply with specifications
2. S.V.P denotes soil vent pipe and to be provided at the head of the drainage
3. Where drainage is shown under driveways and slabs, to be encased in 150mm thick concrete surround.
4. All underground foul and waste drain pipes shall be of PVC to comply with BS5255
5. All ICs within building area driveway and parking to have heavy duty, double-seal airtight covers and walls to be 200mm.
6. Minimum slope in the drain pipes to be 1%
7. No chases for pipes will be allowed in the slabs
8. Sleeves will be allowed with written approval from S.E.
9. No cutting of concrete without express approval of the Architect or S.E
10. All testing of pipes must be coordinated with electrical and any conflicts must be resolved before works begin
11. Permanent vents denoted as P.V to be provided as shown on plan.

ELECTRICAL

All conduits must be laid before plastering

PROJECT:

BUILDING CAPACITY TO DELIVER SKILLS PROGRAMMES FOR THE AGRICULTURAL VALUE CHAIN(AGSKILLS)

CLIENT:

Name: KISII NATIONAL POLYTECHNIC

Signature: _____ Date: _____

DRAWING TITLE:

A.01.1 SITE PLAN

SCALE:

1:500

DRAWN BY:

ARCH. M.V. K.O

CHECKED BY:

Name: ARCH. D.K.K

Signature: _____ Date: _____

DATE: 04/06/2026

